



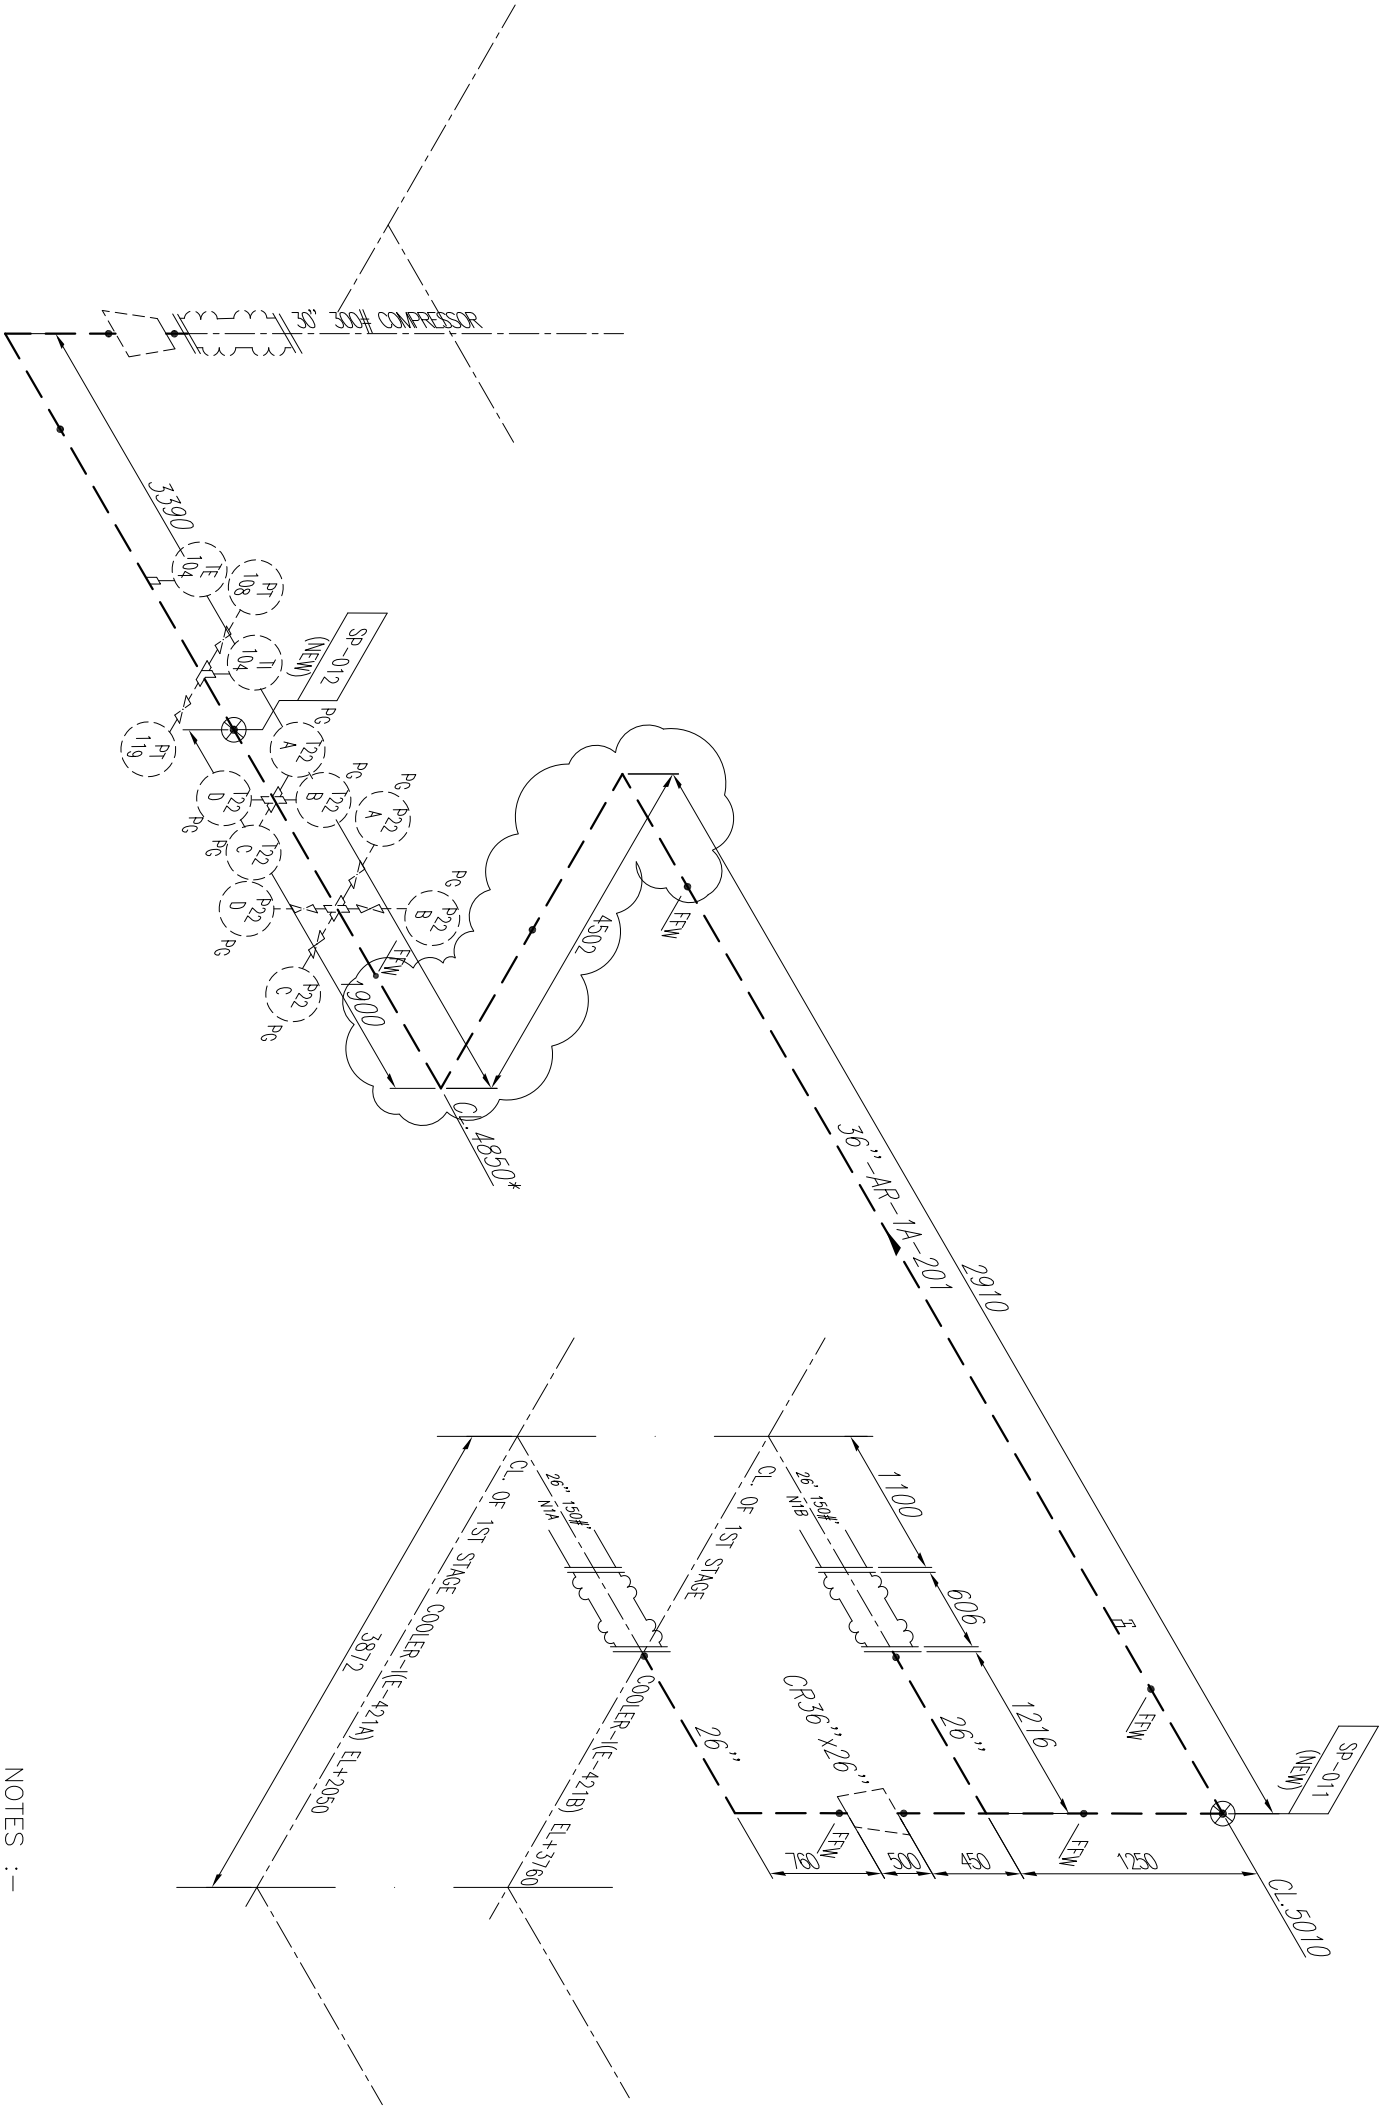

- NOTES :-
1. ALL DIMENSIONS & ELEVATIONS ARE IN mm, UNLESS OTHERWISE SPECIFIED.
 2. ALL FLANGE HOLE TO BE OFF CENTER.
 3. LINE 1 1/2" AND SMALLER , DIMENSION AND ROUTING ARE APPROX. AND TO BE CHECKED AND SUPPORTED IN FIELD
 4. END TO END DIMENSION OF VALVES,CONTROL VALVES,SPECIALITY COMPONENTS ARE TO BE VERIFIED AS PER MANUFACTURE'S STD. BEFORE MARKING OF SPOOL PIECES.
 5. CONTRACTOR SHALL PHYSICALLY CHECK THE ROUTING OF PIPE LINE AND FOULING AT SITE BEFORE STARTING PRE-FABRICATION,
 6. FIELD WELD TO BE DECIDED BY THE FABRICATOR/CONTRACTOR AND ALLOWANCE FOR SITE ADJUSTMENT SHALL BE PROVIDED.
 7. IN CASE OF DISCREPANCY BETWEEN LINE LIST & PROCESS DATA REPORTED ON ISOMETRICS, LINE LIST PREVAILS.
 8. * INDICATES HOLD.

THIS DRAWING IS THE PROPERTY OF PROJECTS & DEVELOPMENT INDIA LTD. AND CAN NEITHER BE COPIED NOR REPRODUCED NOR SHOWN TO THE THIRD PARTIES WITHOUT THE WRITTEN PERMISSION OF PDIL.											
									PRESS.	TEMP.	INSULATION
									(KG/CM ² G)	(°C)	TYPE THK(mm)
0	30.12.25	ISSUED	AK	BKC	DD	OPERAT.	3.21	208	H	80	
REV	DATE	DESCRIPTION	DRN.	CKD.	APPD.	DESIGN	4	249			

PROJECTS & DEVELOPMENT INDIA LTD.NOIDA

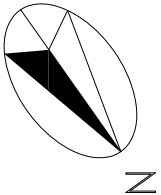

CLIENT:- M/S YARA FERTILISERS INDIA PVT LTD

PROJECT:-BASIC ENG.DETAIL ENG. & FLEXIBILITY ANALYSIS FOR VARIOUS SAFETY,PLANT OPERATION SUBSTANCE & ESP. (UPGRADATION OF E-421: AMMONIA PLANT AIR COMPRESSOR 1ST INTERSTAGE EXCHANGER)

P&ID No.	PIPING PLAN NO.	PIPE SUB.NO.	DRAWING NO.			SH	1	OF	1
—	0603	—	EM37400000	6300	AR	201			